


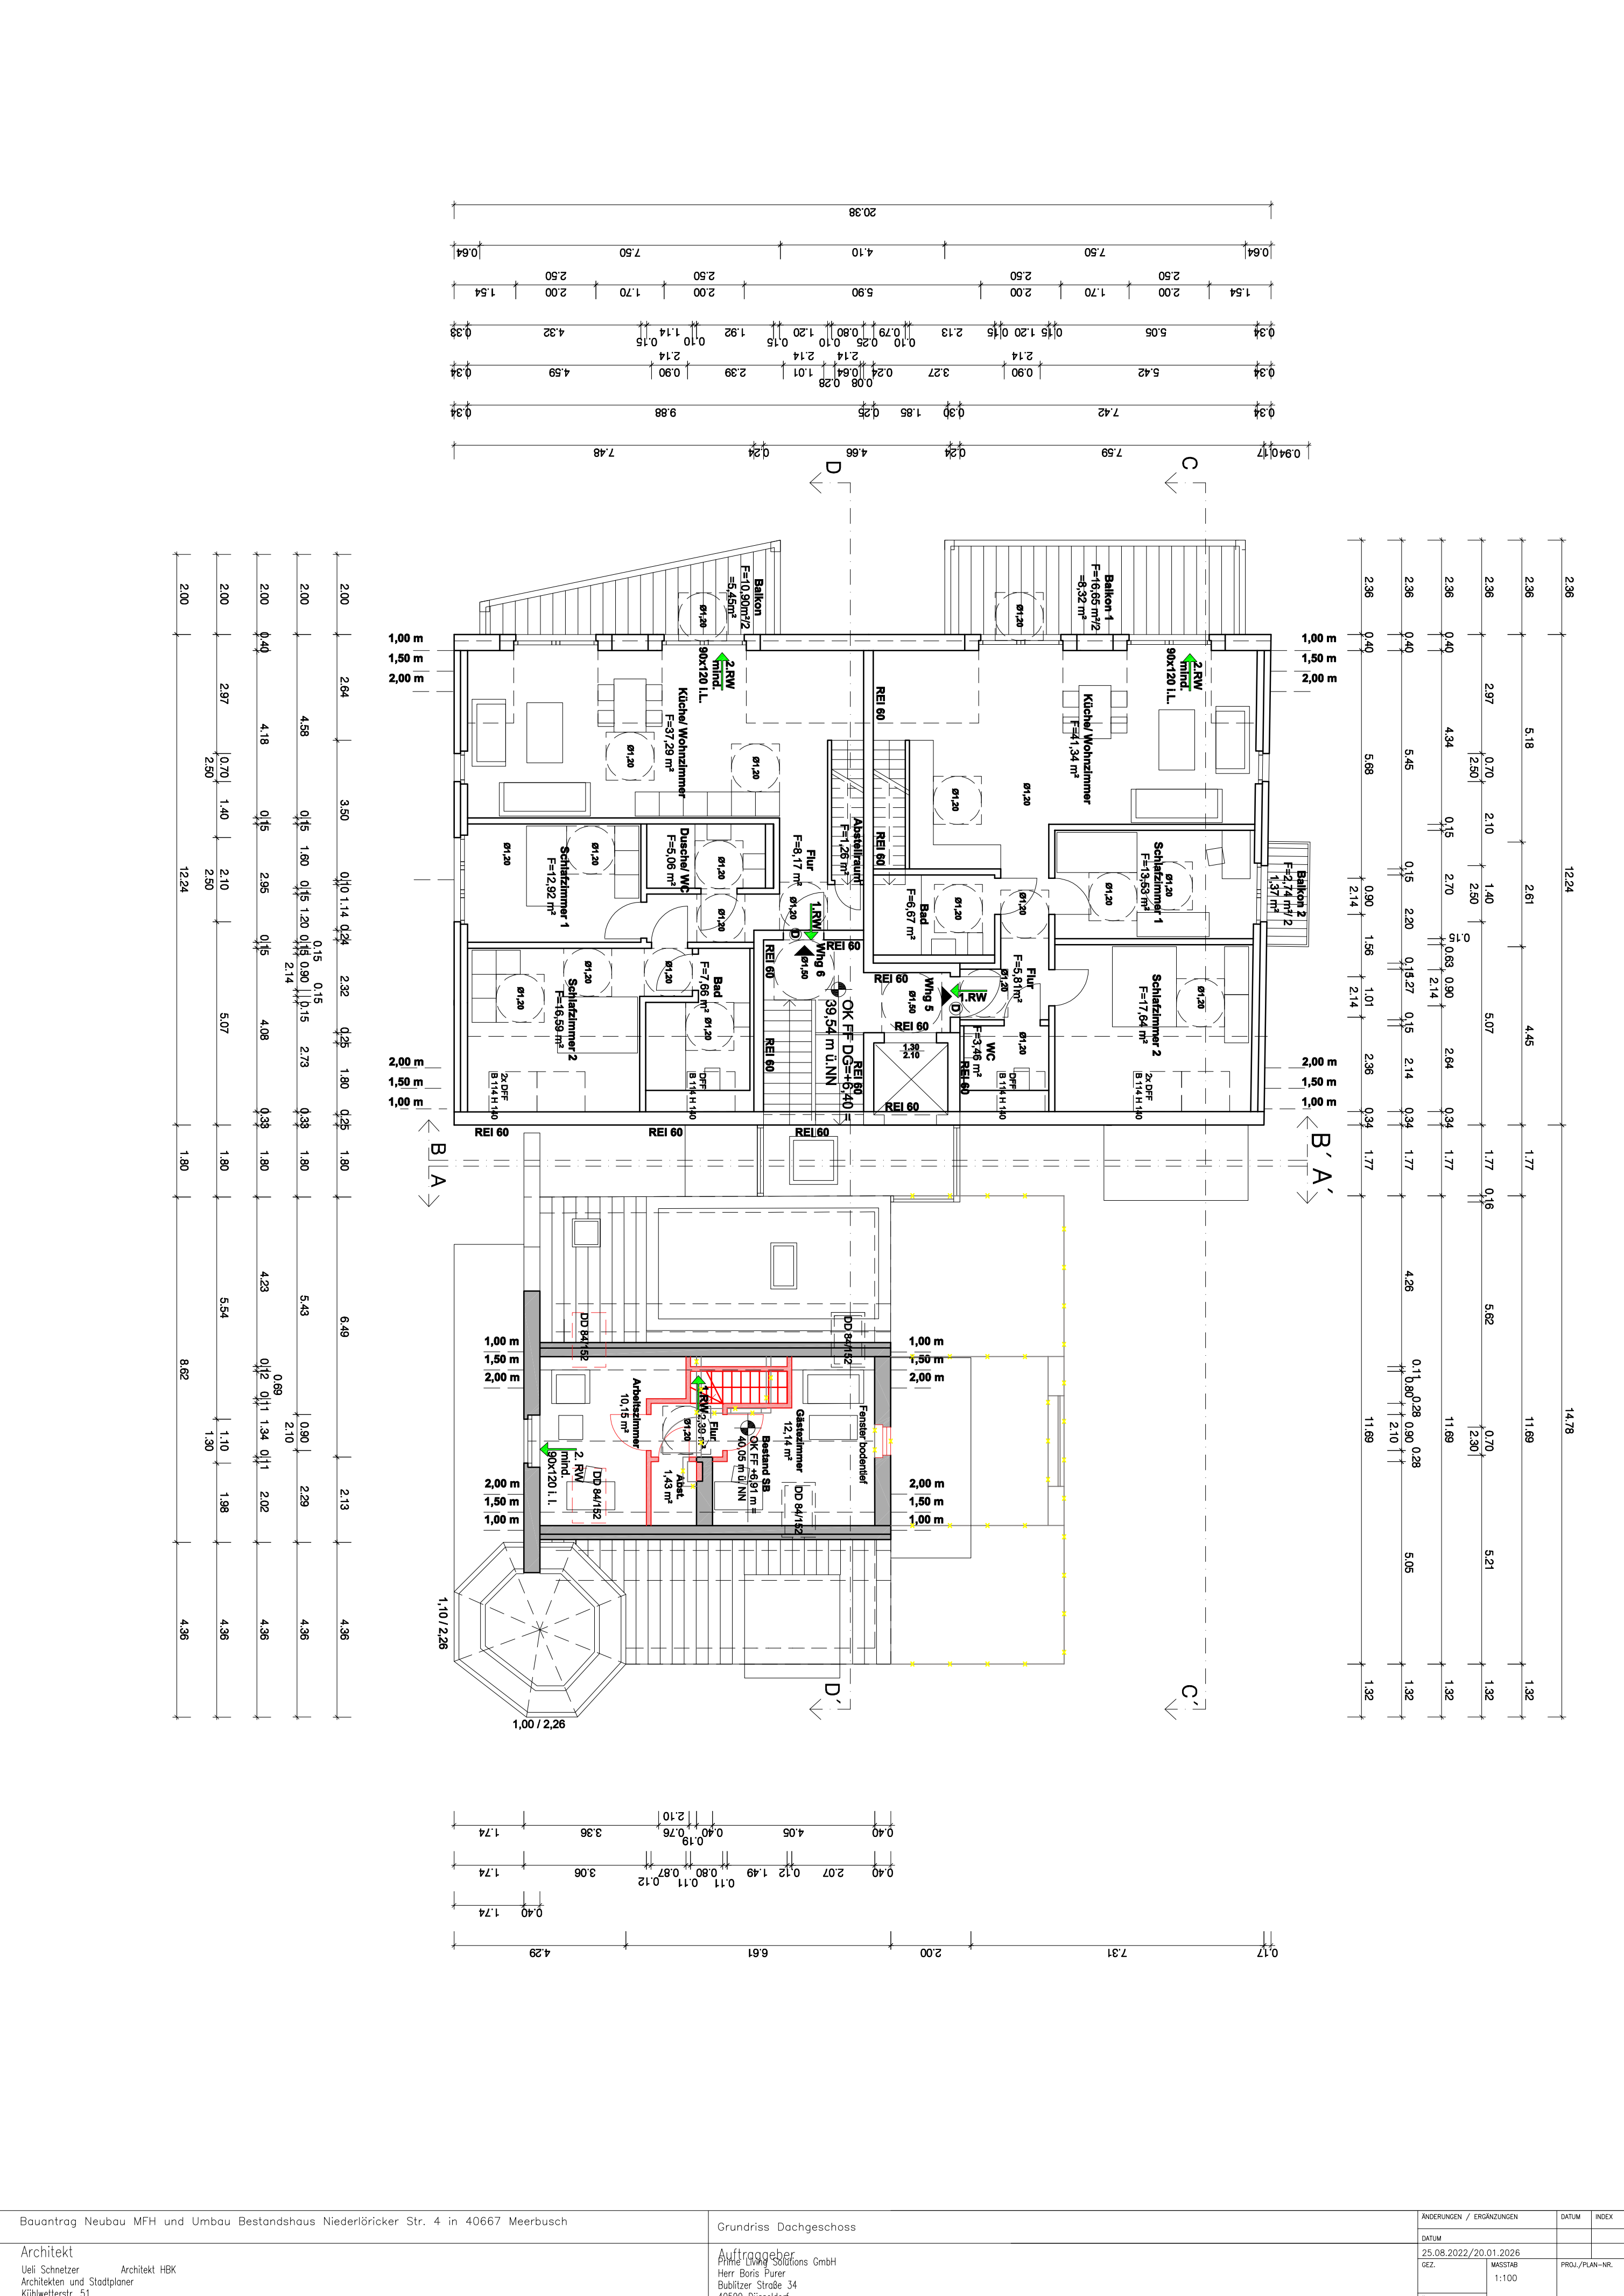

ÄNDERUNGEN / ERGÄNZUNGEN		DATUM	INDEX
25.08.2022/20.01.2026			
GEZ.	MASSTAB	PROJ./PLAN-NR.	
AND.	1:100		

Bauantrag Neubau MFH und Umbau Bestandshaus Niederlörcker Str. 4 in 40667 Meerbusch		Grundriss Dachgeschoss	
Architekt Ueli Schnetzer Architekten und Stadtplaner Kühlwetterstr. 51 40239 Düsseldorf		Auftraggeber Prime Living Solutions GmbH Herr Boris Purer Bublitzer Straße 34 40599 Düsseldorf	