


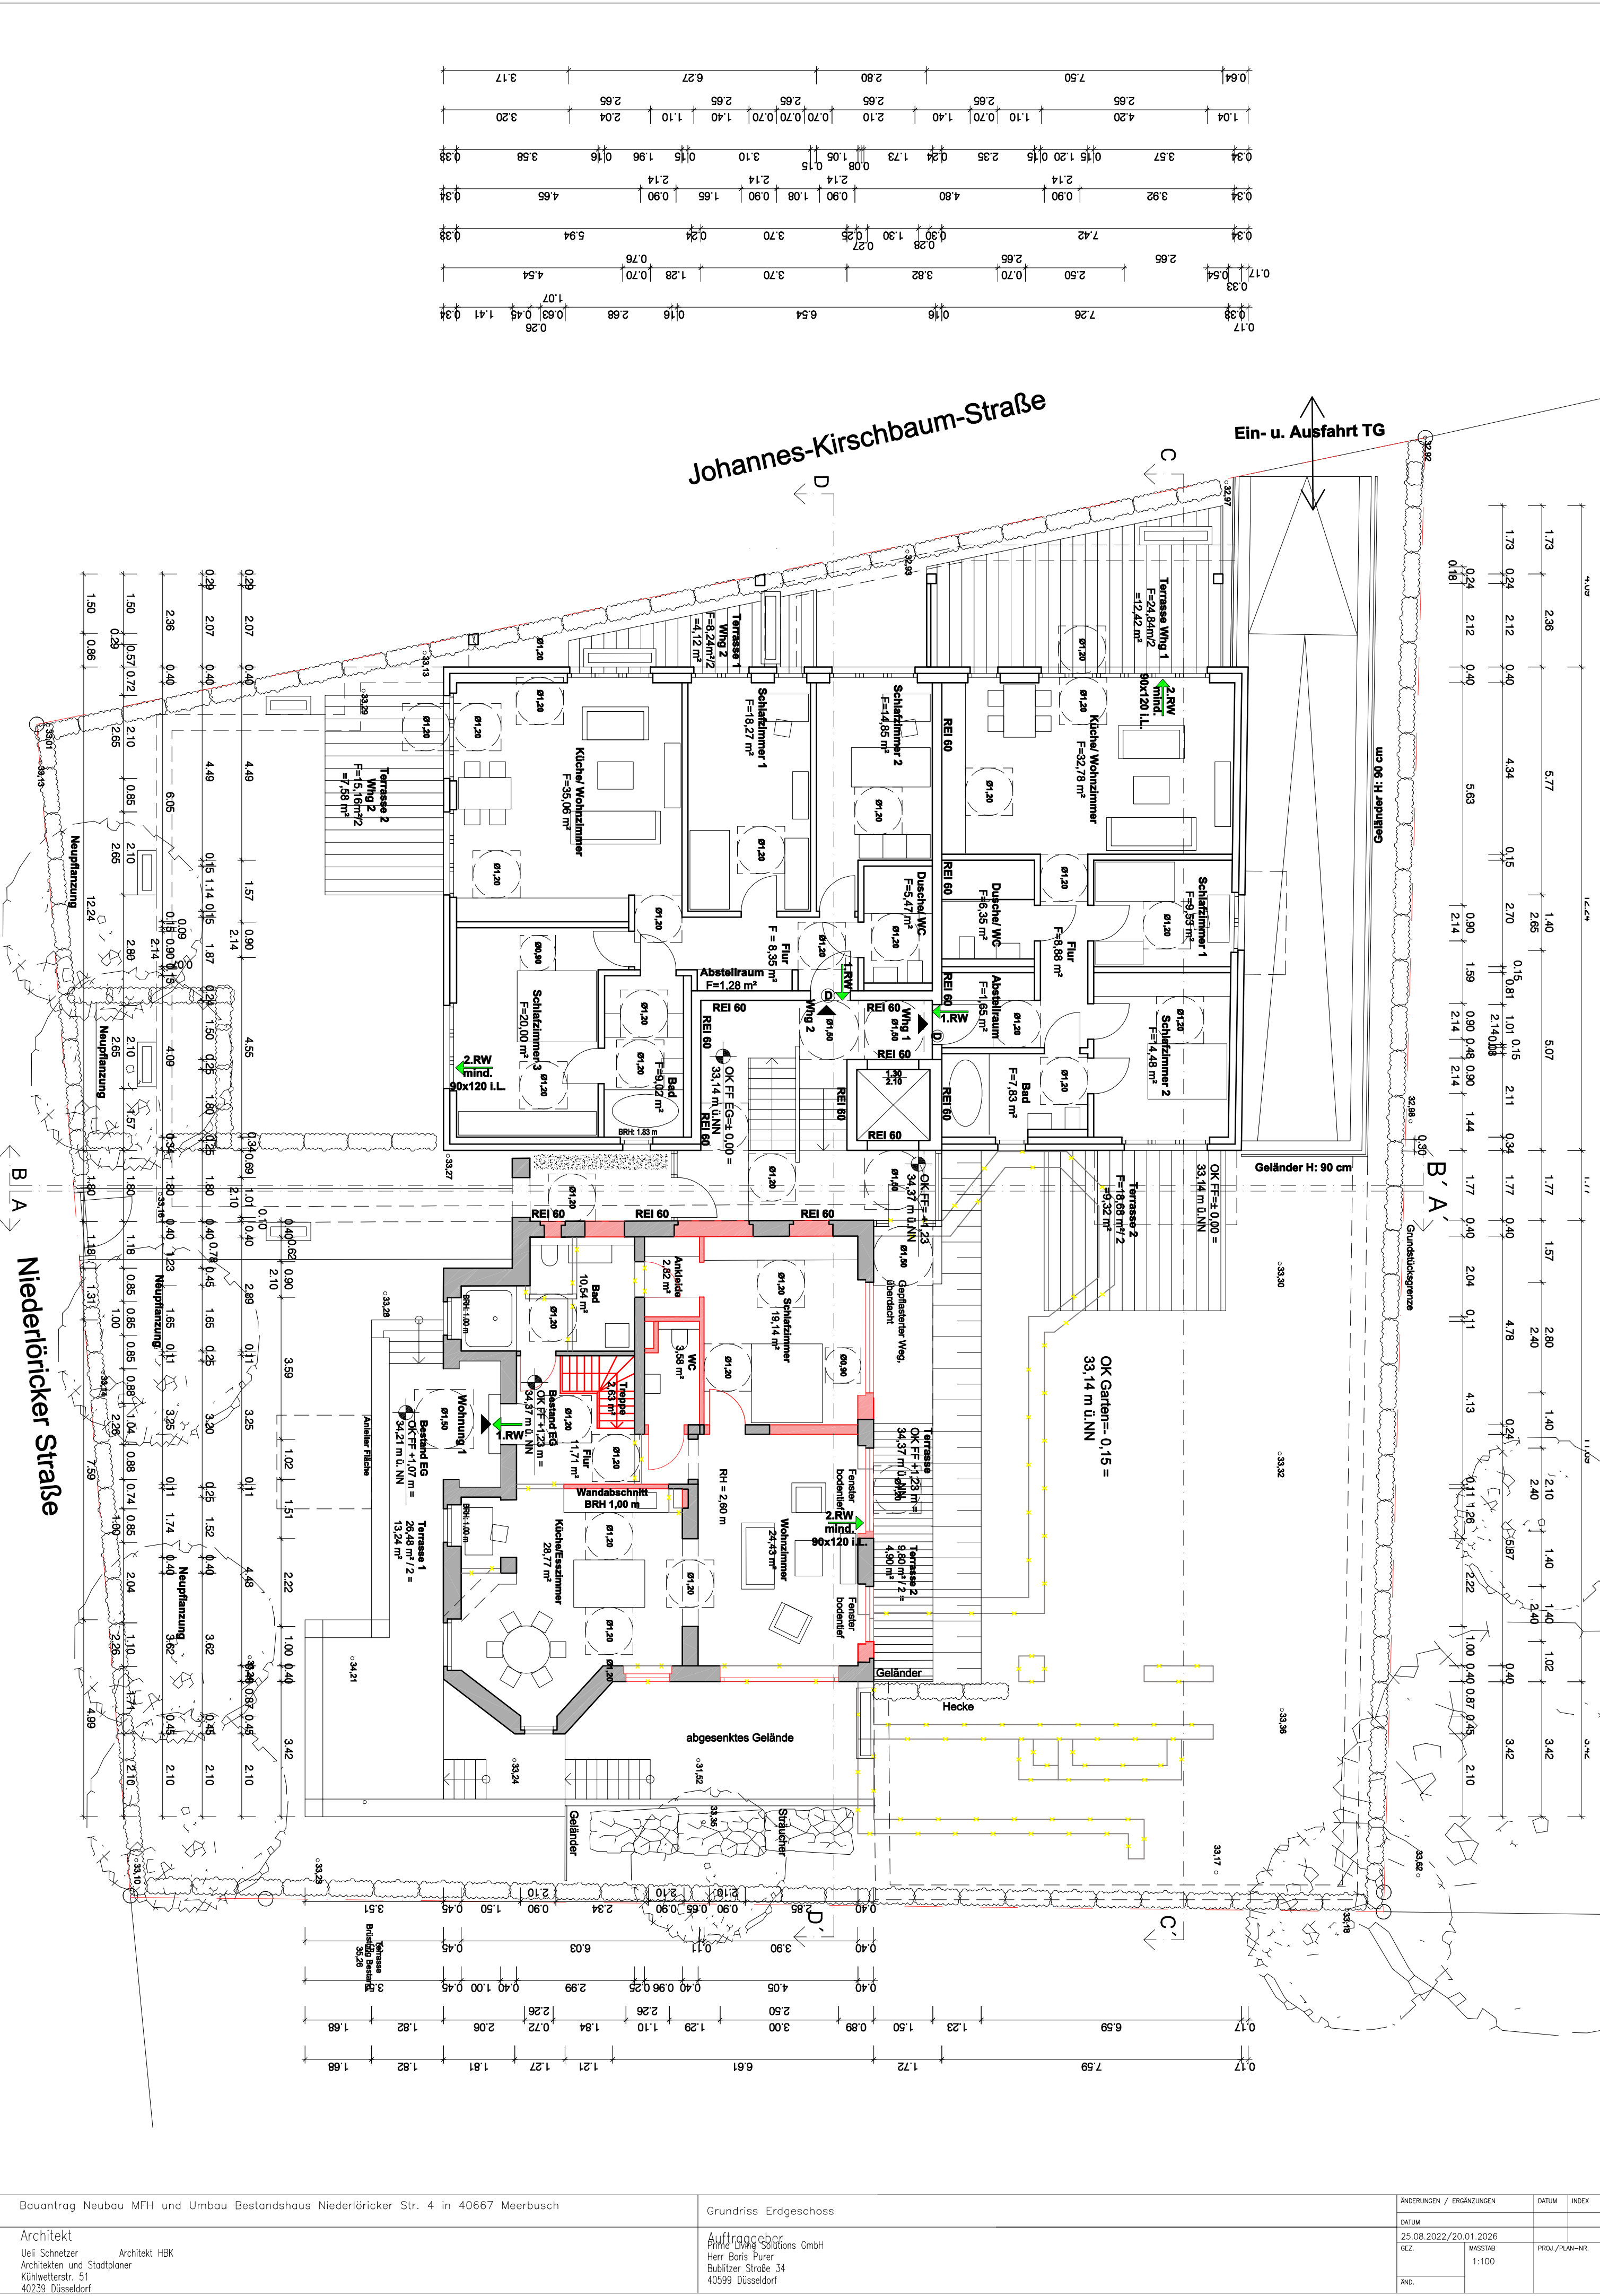

ÄNDERUNGEN / ERGÄNZUNGEN		DATUM	INDEX
DATUM		25.08.2022/20.01.2026	
GEZ.		MASSSTAB	PROJ./PLAN-NR.
AND.		1:100	

Bauantrag Neubau MFH und Umbau Bestandshaus Niederlörcker Str. 4 in 40667 Meerbusch		Grundriss Erdgeschoss	
Architekt		Auftraggeber	
Ueli Schnetzer Architekt HBK		Prime Living Solutions GmbH	
Architekten und Stadtplaner		Herr Boris Purer	
Kühlwetterstr. 51		Bublitzer Straße 34	
40239 Düsseldorf		40599 Düsseldorf	