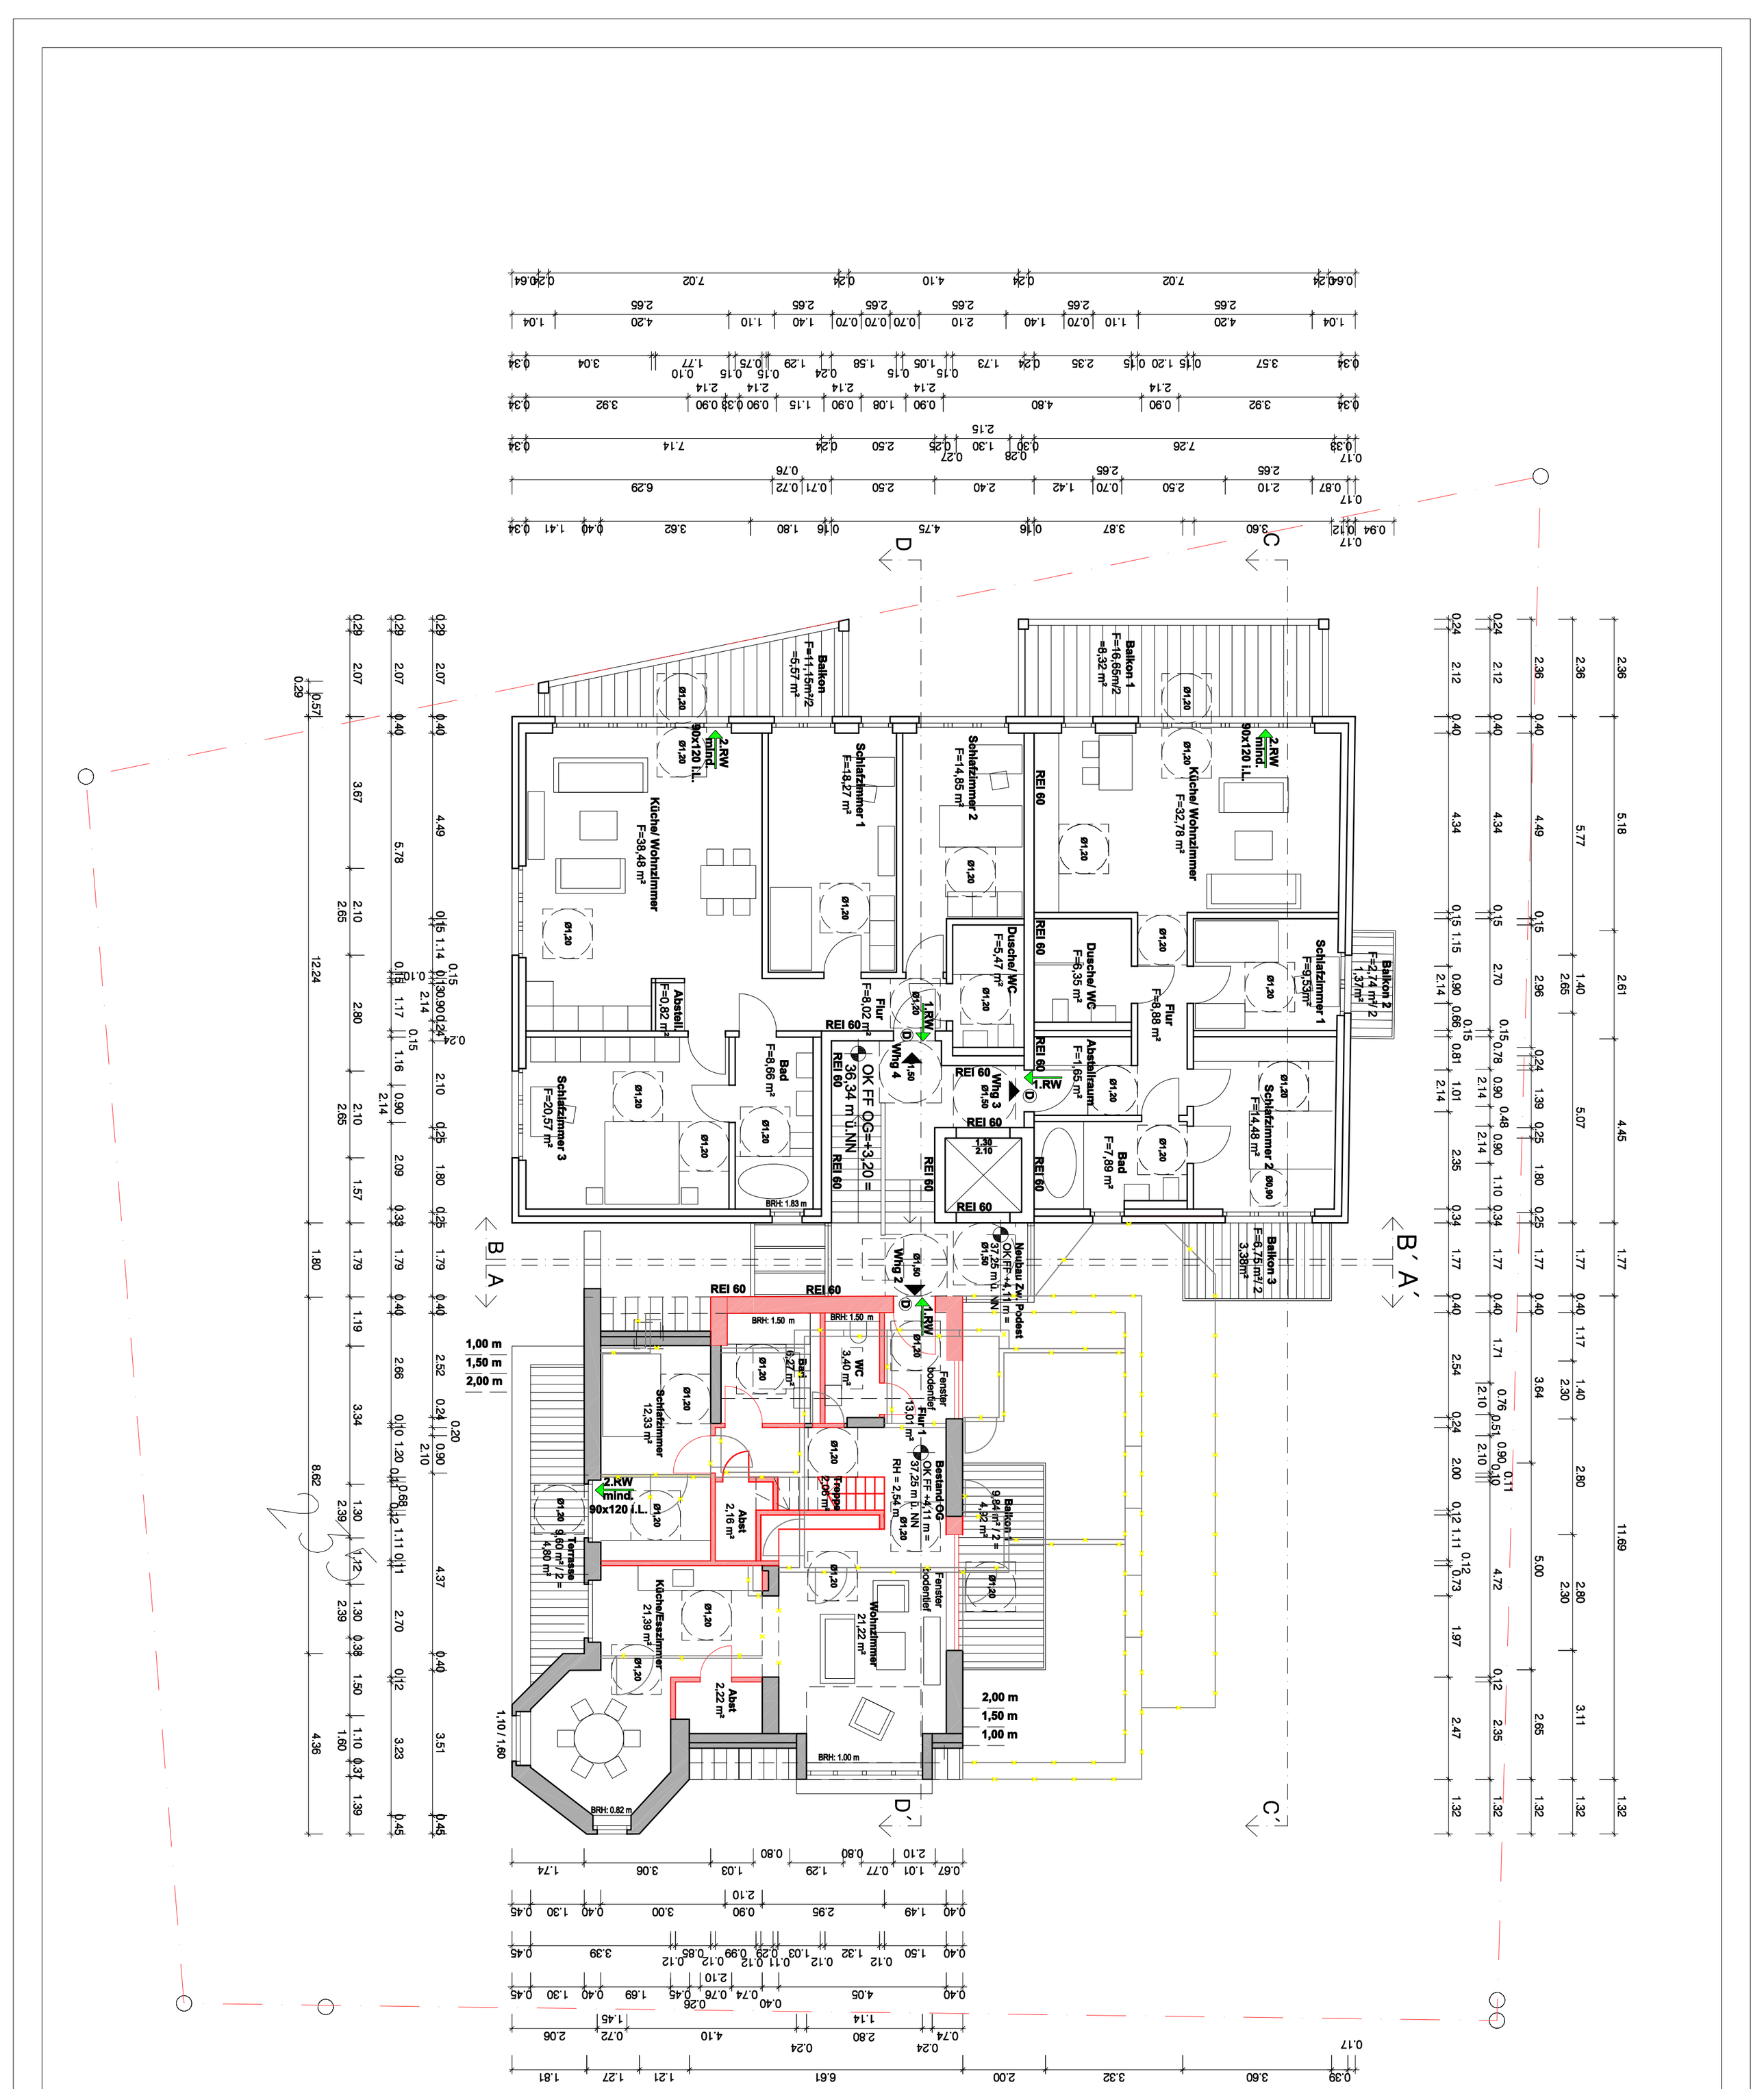

Bauantrag Neubau MFH und Umbau Bestandshaus Niederlöricker Str. 4 in 40667 Meerbusch	Grundriss 1. Obergeschoss	ÄNDERUNGEN / ERGÄNZUNGEN	DATUM / INDEX
		DATUM: 25.08.2022/20.01.2026	
Architekt Ueli Schnetzer Architekt HBK Architekten und Stadtplaner Kühlwetterstr. 51 40239 Düsseldorf	Auftraggeber Prime Living Solutions GmbH Herr Boris Purer Bublitzer Straße 34 40599 Düsseldorf	GEZ. / ÄND.	MASSTAB 1:100 / PROJ./PLAN–NR.