


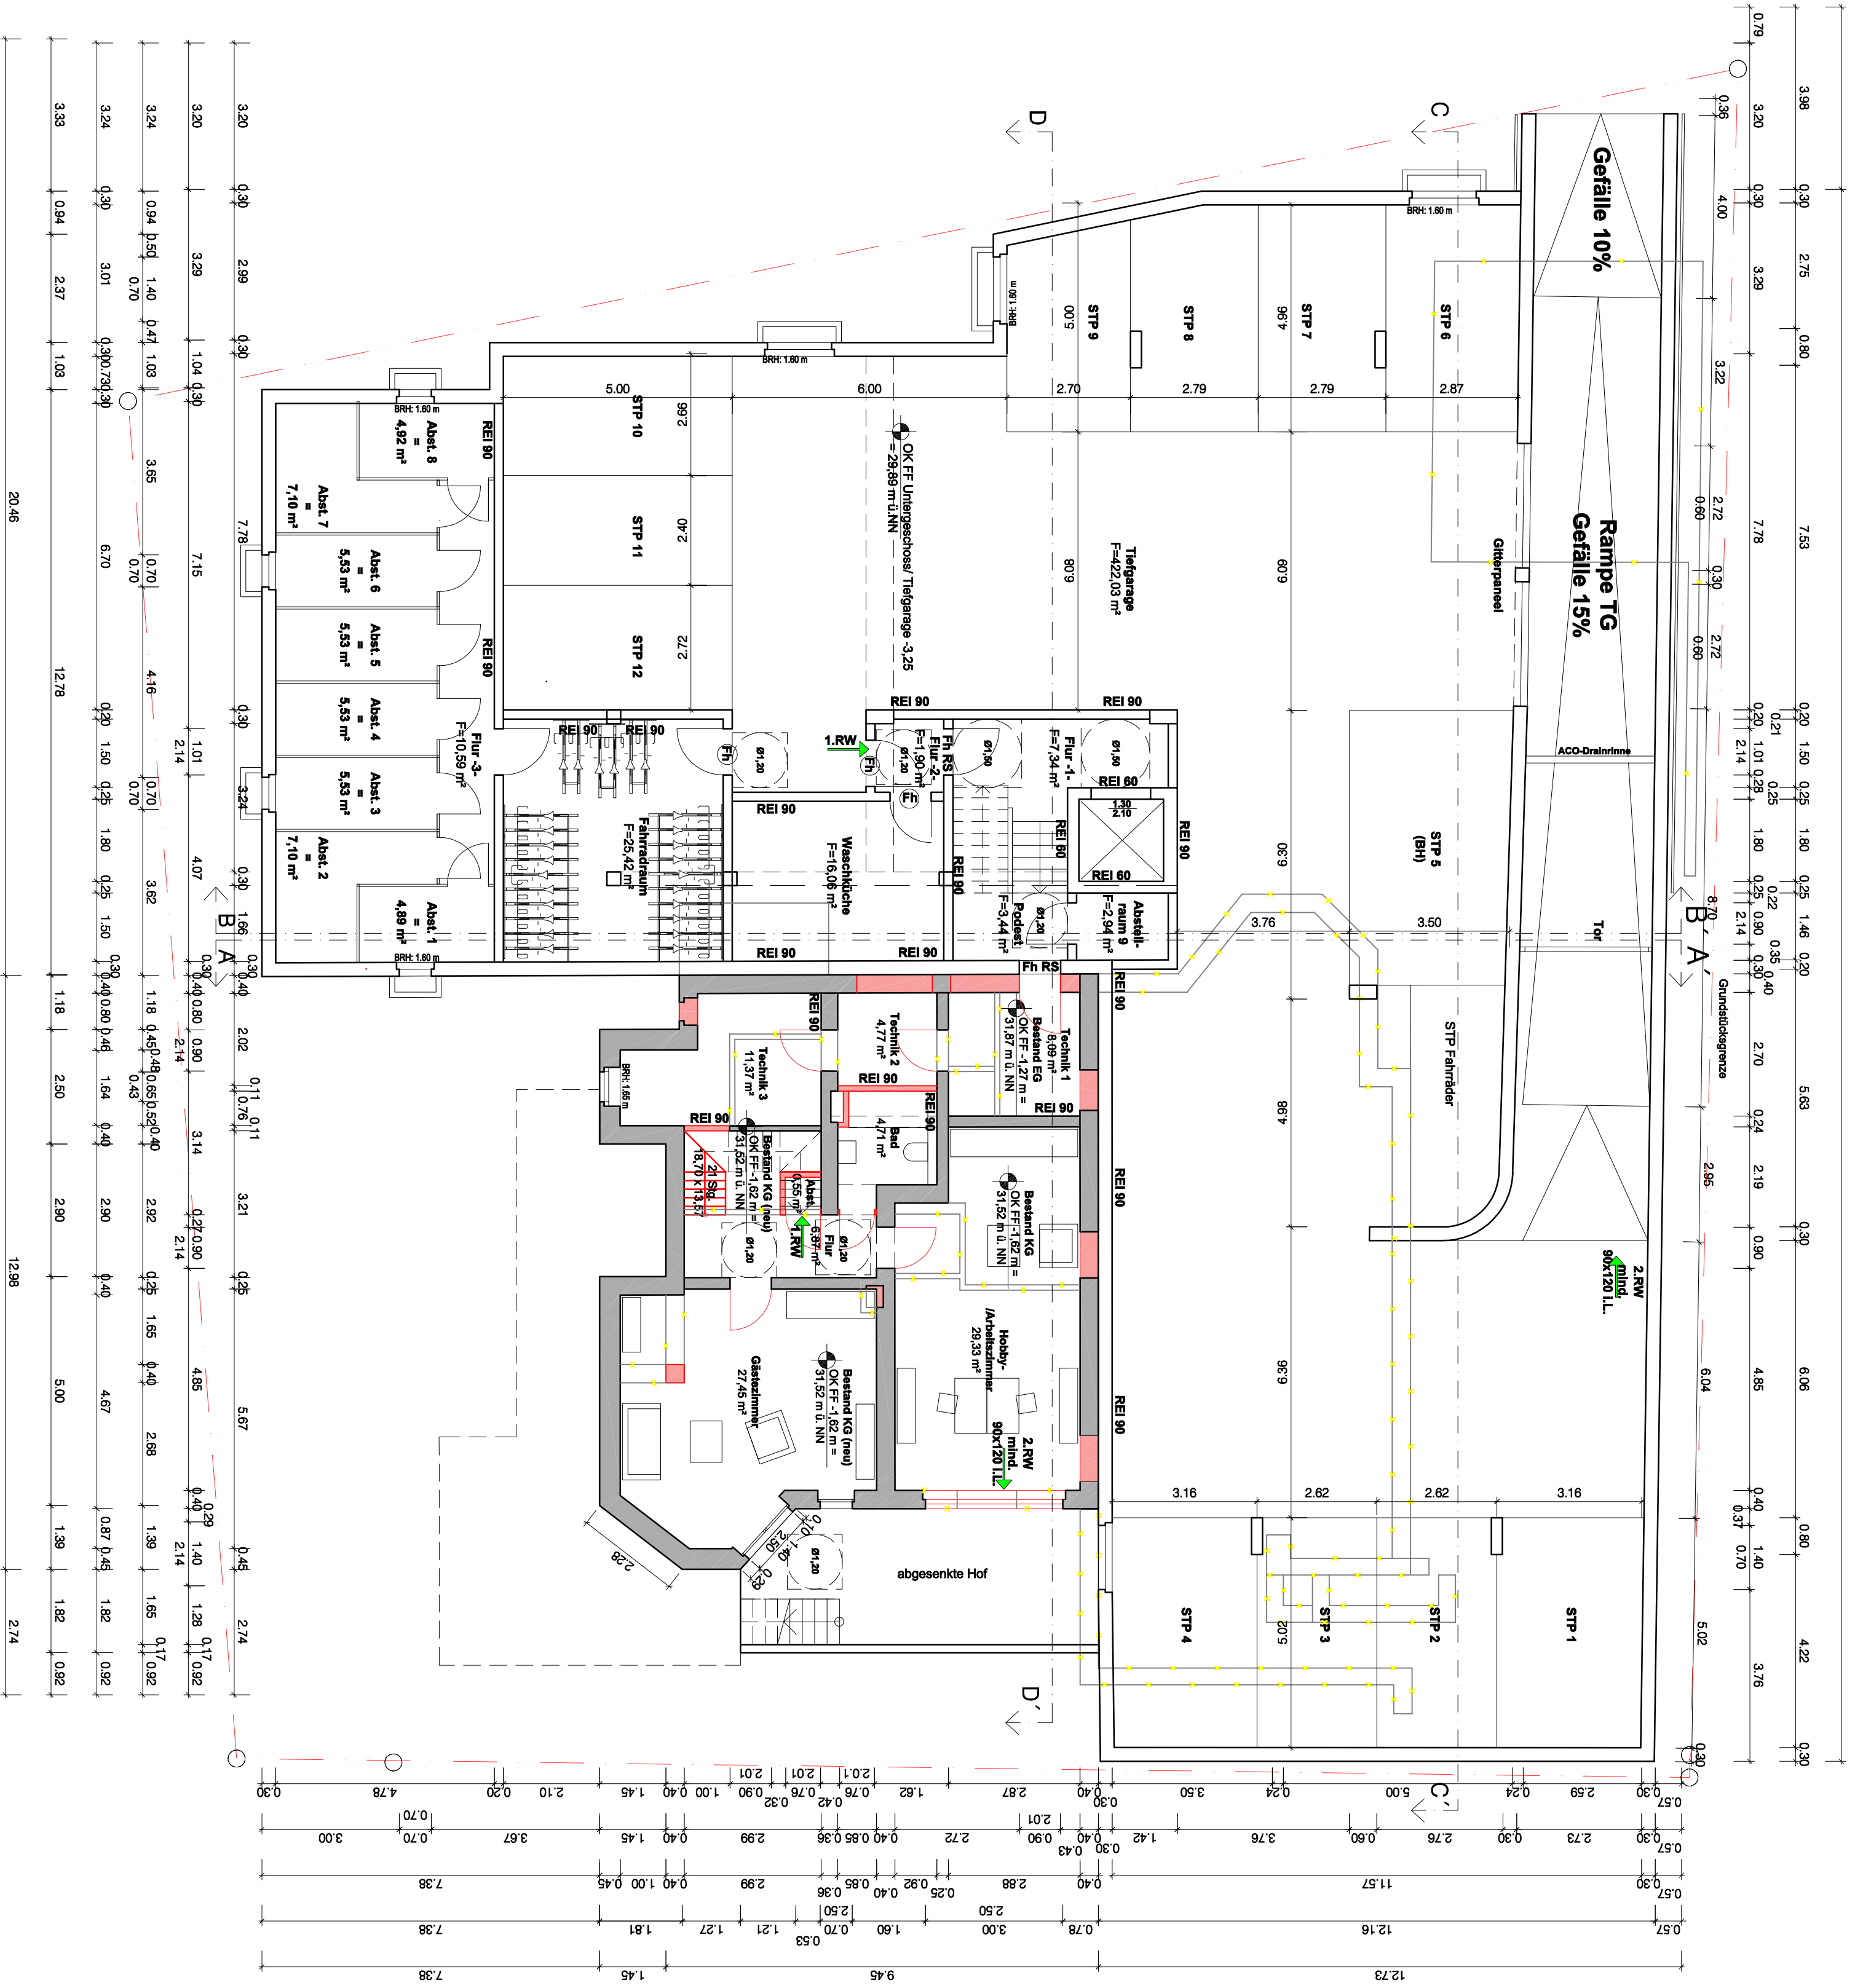

ÄNDERUNGEN / ERGÄNZUNGEN		DATUM	INDEX
DATUM		25.08.2022/20.01.2026	
GEZ.		MASSSTAB	PROJ./PLAN-NR.
AND.		1:100	

Bauantrag Neubau MFH und Umbau Bestandshaus Niederlöricker Str. 4 in 40667 Meerbusch		Grundriss Untergeschoss
Architekt Ueli Schnetzer Architekten und Stadtplaner Kühlwetterstr. 51 40239 Düsseldorf		Auftraggeber Prime Living Solutions GmbH Herr Boris Purer Bublitzer Straße 34 40599 Düsseldorf